

CONCEPT IMAGE — ILLUSTRATIVE ONLY. Massing, height, materials and exterior color (LRV ≤ 38) are governed by these drawings, not by the image.

JOSHMAHAL

A RAJASTHANI PALACE ON MUMMY MOUNTAIN

PRIVATE RESIDENCE · 7080 N INVERGORDON RD · PARADISE VALLEY, ARIZONA

SCHEMATIC DESIGN SET · SD-01 · OCT 18, 2026

PROJECT DATA	
Address	7080 N Invergordon Rd, Paradise Valley AZ 85253
Assessor parcel	169-01-003D · Maricopa County
Lot area	225,151 sf (5.17 ac) per Assessor
Jurisdiction	Town of Paradise Valley
Zoning	R-43 single-family, Hillside Development Area — VERIFY
Use / occupancy	Single-family residence (IRC) — VERIFY
Construction	Conc./CMU + stone veneer; fire sprinklered — VERIFY
Levels	Lower (F.F. 1,672.00') + Main (F.F. 1,685.00')
Conditioned area	11,890 sf (main 5,982 · lower 5,908)
Garage	816 sf · 4 cars (tandem)
Bedroom suites	4 (primary, suite 2, guest 3, guest 4)
Overall height	37'-6" (40'-0" max.) · 24' plane: complies
Disturbed area	15,928 sf (7.1% of lot)

SHEET INDEX

G-001	COVER SHEET
G-002	ZONING, HILLSIDE & AREA ANALYSIS
AS-101	ARCHITECTURAL SITE PLAN
AS-102	ENLARGED SITE PLAN — SUMMIT
A-101	LOWER LEVEL FLOOR PLAN
A-102	MAIN LEVEL FLOOR PLAN
A-103	ROOF PLAN
A-201	EXTERIOR ELEVATIONS
A-202	EXTERIOR ELEVATIONS
A-301	BUILDING SECTIONS
A-501	EXTERIOR DETAILS
A-601	SCHEDULES

PROJECT TEAM

OWNERLandmark Venture Group LLC — Sarvesh Joshi, Managing Partner

ARCH. Arizona-registered architect — to be engaged

SURVEYALTA / topographic survey — to be engaged

CIVIL Grading, drainage, on-site wastewater — to be engaged

GEO. Geotechnical investigation (rock excavation) — to be engaged

STRUCTStructural engineer — to be engaged


DATA SOURCES

Parcel boundary, area & neighbors: Maricopa County Assessor GIS parcel service, queried 10/18/2026.

Terrain: 32 spot elevations from USGS 3DEP 1-m LiDAR (Elevation Point Query Service), NAVD88 ft; contours interpolated (thin-plate spline).

Hillside standards: Town of Paradise Valley Zoning Ordinance Art. XXII and Hillside application/height-certification packets.

VICINITY — ADJACENT PARCELS

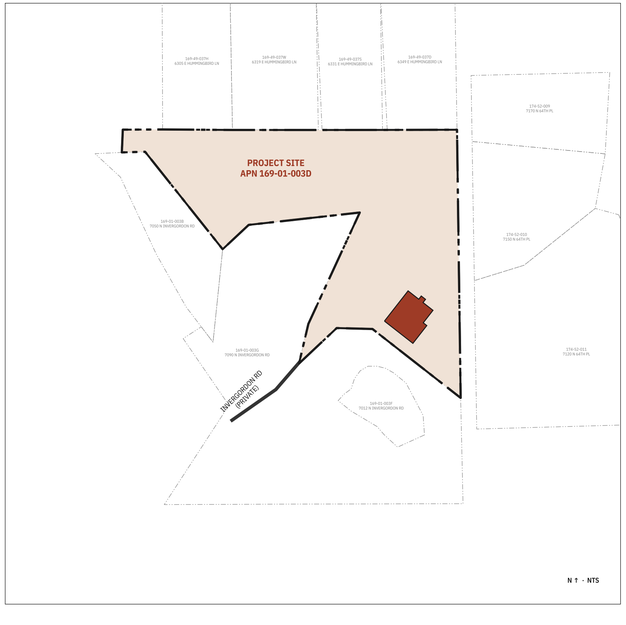

SYMBOLS

- A — COLUMN GRID
- 1 / A-301 — SECTION / ELEVATION MARKER
- 207 — ROOM NUMBER
- ELEVATION DATUM
- 24'-0" HEIGHT PLANE
- NATURAL GRADE (PRE-DEVELOPMENT)
- PROPERTY LINE
- LIMIT OF DISTURBANCE
- STONE / CONC. WALL (CUT)
- +1,687.7 — LIDAR SPOT ELEVATION

ABBREVIATIONS

A.F.F.	ABOVE FINISHED FLOOR
CLG.	CEILING
EL.	ELEVATION (NAVD88)
F.F.	FINISHED FLOOR
LRV	LIGHT REFLECTANCE VALUE
NTS	NOT TO SCALE
SS	STAINLESS STEEL
T.O.	TOP OF
TYP.	TYPICAL
VERIFY	CONFIRM WITH AUTHORITY / SURVEY

GENERAL NOTES

1. This set is a schematic design study prepared for the owner. It is not prepared, sealed or signed by an Arizona registrant and may not be used for permit, bidding or construction.
2. Boundary is taken from county GIS, not a boundary survey. Obtain an ALTA/NSPS survey with topography at 1'-0" contours before design development.
3. Terrain is interpolated from 32 LiDAR points. Building placement, floor elevations, height-plane and disturbance figures shall be recomputed from the certified topographic survey.
4. Hillside Building Committee review and approval is required before a building permit. Zoning, setbacks, disturbance allowance, cut/fill and retaining limits to be confirmed with the Town.
5. No municipal sewer: an engineered on-site wastewater system is required; percolation testing and county permits by civil engineer.
6. Exterior materials and colors shall not exceed LRV 38; outdoor lighting shall be shielded and comply with the Town's hillside lighting standards.

Landmark VENTURE GROUP

OWNER / DEVELOPER

LANDMARK VENTURE GROUP LLC

Sarvesh Joshi, Managing Partner

Paradise Valley, Arizona

sarvesh@landmarkdigi.com

ARCHITECT OF RECORD

TO BE ENGAGED — ARIZONA-REGISTERED

ARCHITECT (A.R.S. §32-101 et seq.)

NO SEAL

SCHEMATIC STUDY

NOT A REGISTRANT'S DOCUMENT

CONSULTANTS (TO BE ENGAGED)

SURVEY — ALTA / TOPOGRAPHIC

CIVIL — GRADING, DRAINAGE, ON-SITE WASTEWATER

GEOTECHNICAL

STRUCTURAL

MEP / FIRE PROTECTION

LANDSCAPE — NATIVE REVEGETATION

JOSHMAHAL

PRIVATE RESIDENCE

7080 N INVERGORDON ROAD

PARADISE VALLEY, ARIZONA 85253

APN 169-01-003D · 225,151 SF (5.17 AC)

ISSUES / REVISIONS

NO.	DATE	DESCRIPTION
0	10/18/26	SCHEMATIC DESIGN — SD-01


PHASE

SCHEMATIC DESIGN

DATE OCT 18, 2026 — PROJECT JM-2610

DRAWN LVG — CHECKED —

KEY PLAN

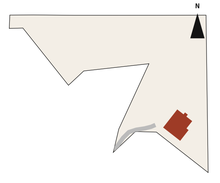

SHEET TITLE

COVER SHEET

SCALE: AS NOTED

SHEET

G-001

1 OF 12

NOT FOR CONSTRUCTION

NOT FOR PERMIT · NOT FOR BIDDING

SCHEMATIC DESIGN — FOR OWNER REVIEW

© 2026 Landmark Venture Group LLC · JM-2610 · G-001

SLOPE ANALYSIS (PRE-DEVELOPMENT)



1 SLOPE ANALYSIS MAP

1" = 60'-0" - FROM USGS 3DEP LIDAR (INTERPOLATED)

SLOPE BANDS (WITHIN PARCEL)

SLOPE	AREA (SF)	SHARE
0–15%	1,184	1%
15–25%	10,912	5%
25–35%	21,488	10%
35–50%	75,808	34%
50%+	110,928	50%

AVERAGE SLOPE

Standard Arizona hillside formula S = 0.0023 × I × L ÷ A, with I = 2 ft contour interval, L = 55,139 ft of 2-ft contours inside the parcel, A = 5.17 ac.

S = 49% average lot slope (gradient method: 50%). Building-site area (summit) = 39%.

Use the Town's adopted method and table on the certified survey; these are planning estimates.

HILLSIDE & ZONING COMPLIANCE SUMMARY (SCHEMATIC)

STANDARD	LIMIT	THIS DESIGN	STATUS
Building height, primary	24'-0" plane parallel to natural grade	Complies — min. margin 4" at NE corner	OK*
Overall height	40'-0" lowest built point to highest	37'-6" (EL. 1,671.5' → 1,709.0')	OK
Exposed vertical face	24'-0" from lowest finished grade	16'-6" max. (west, stepped terrace)	OK
Accessory structures	16'-0" above natural grade	None proposed (guest suites internal)	N/A
Exterior color	LRV ≤ 38%	Rose-red sandstone, target LRV ≤ 32	OK
Disturbed area	Per Town slope table	15,928 sf = 7.1% of lot	VERIFY
Retaining walls	8'-0" max. exposed (verify)	Tiered ≤ 8'-0" each (SW garden, motor court)	OK
Floor area / coverage	25% of lot (verify)	11,964 sf footprint+floor = 5.6%	OK
Setbacks	20'-0" min. assumed all lines (verify)	Building ≥ 20'-0" from every lot line	OK
Outdoor lighting	Shielded, hillside standards	Shielded lanterns only; no façade uplight	OK

* Tightest point is the NE parapet corner (grade = 1,675.3'). If the survey shows lower grade, drop the NE parapet 12" or step the corner.

24-FT PLANE CHECK AT KEY ELEMENTS (NATURAL GRADE FROM LIDAR SURFACE)

ELEMENT	NAT. GRADE	PLANE EL.	TOP EL.	MARGIN
Dome finial (great hall)	1,689.9	1,713.9	1,709.0	+4.9'
Chhatri 1 finial	1,686.3	1,710.3	1,708.5	+1.8'
Chhatri 2 finial	1,688.8	1,712.8	1,708.5	+4.3'
Chhatri 3 finial	1,686.4	1,710.4	1,708.5	+1.9'
Chhatri 4 finial	1,687.4	1,711.4	1,708.5	+2.9'
Mandir shikhara finial	1,686.0	1,710.0	1,703.6	+6.4'
Parapet corner (10,30)	1,686.1	1,710.1	1,699.0	+11.1'
Parapet corner (90,30)	1,687.3	1,711.3	1,699.0	+12.3'
Parapet corner (90,80)	1,677.0	1,701.0	1,699.0	+2.0'
Parapet corner (80,80)	1,682.4	1,706.4	1,699.0	+7.4'
Parapet corner (80,115)	1,675.7	1,699.7	1,699.0	+0.7'
Parapet corner (52,115)	1,687.8	1,711.8	1,699.0	+12.8'
Parapet corner (52,124)	1,683.7	1,707.7	1,699.0	+8.7'
Parapet corner (40,124)	1,683.5	1,707.5	1,699.0	+8.5'
Parapet corner (40,115)	1,687.1	1,711.1	1,699.0	+12.1'
Parapet corner (10,115)	1,678.0	1,702.0	1,699.0	+3.0'

AREA TABULATION

AREA	GROSS SF	NET SF
MAIN LEVEL	5,982	5,213
LOWER LEVEL	6,724	5,893
LESS GARAGE (LOWER)	-816	
TOTAL CONDITIONED	11,890	
BAOLI COURT (OPEN)	576	
VIEW TERRACE + POOL	584	

DISTURBANCE (EST.)

Building footprints, motor court, sunken garden, terrace, drive (191 ft) plus a 5-ft work zone: 15,928 sf.

Lot 225,151 sf → 7.1%. The Town's table allows a shrinking share as slope rises (+60% at 10%, +34% at 15%, +13% at 25%, +10% at 40%); with a ≈49% average lot slope the allowance is likely single-digit — this design is sized to fit, subject to survey.

VASTU ORIENTATION (TRUE NORTH)



ORIENTATION NOTES

The plan is rotated about 38° so its main axis runs from the SW arrival to the NE view; the building corners point to the cardinal directions.

Open centre (Brahmasthan) = baoli court. NE (Ishanya) = mandir and great hall. SE (Agneya) = kitchen. SW (Nairutya) = primary suite on the highest, heaviest ground.

Entry is from the NW via the motor court (Vayavya). Review with the owner's Vastu consultant.

Landmark VENTURE GROUP

OWNER / DEVELOPER

LANDMARK VENTURE GROUP LLC

Sarvesh Joshi, Managing Partner

Paradise Valley, Arizona

sarvesh@landmarkdigi.com

ARCHITECT OF RECORD

TO BE ENGAGED — ARIZONA-REGISTERED

ARCHITECT (A.R.S. §32-101 et seq.)

NO SEAL

SCHEMATIC STUDY

NOT A REGISTRANT'S DOCUMENT

CONSULTANTS (TO BE ENGAGED)

SURVEY — ALTA / TOPOGRAPHIC

CIVIL — GRADING, DRAINAGE, ON-SITE WASTEWATER

GEOTECHNICAL

STRUCTURAL

MEP / FIRE PROTECTION

LANDSCAPE — NATIVE REVEGETATION

JOSHMAHAL

PRIVATE RESIDENCE

7080 N INVERGORDON ROAD

PARADISE VALLEY, ARIZONA 85253

APN 169-01-003D · 225,151 SF (5.17 AC)

ISSUES / REVISIONS

NO.	DATE	DESCRIPTION
0	10/18/26	SCHEMATIC DESIGN — SD-01


PHASE

SCHEMATIC DESIGN

DATE OCT 18, 2026 PROJECT JM-2610

DRAWN LVG CHECKED —

KEY PLAN

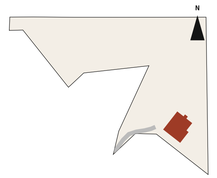

SHEET TITLE

ZONING, HILLSIDE & AREA ANALYSIS

SCALE: AS NOTED

SHEET

G-002


2 OF 12

NOT FOR CONSTRUCTION

NOT FOR PERMIT · NOT FOR BIDDING

SCHEMATIC DESIGN — FOR OWNER REVIEW

© 2026 Landmark Venture Group LLC · JM-2610 · G-002

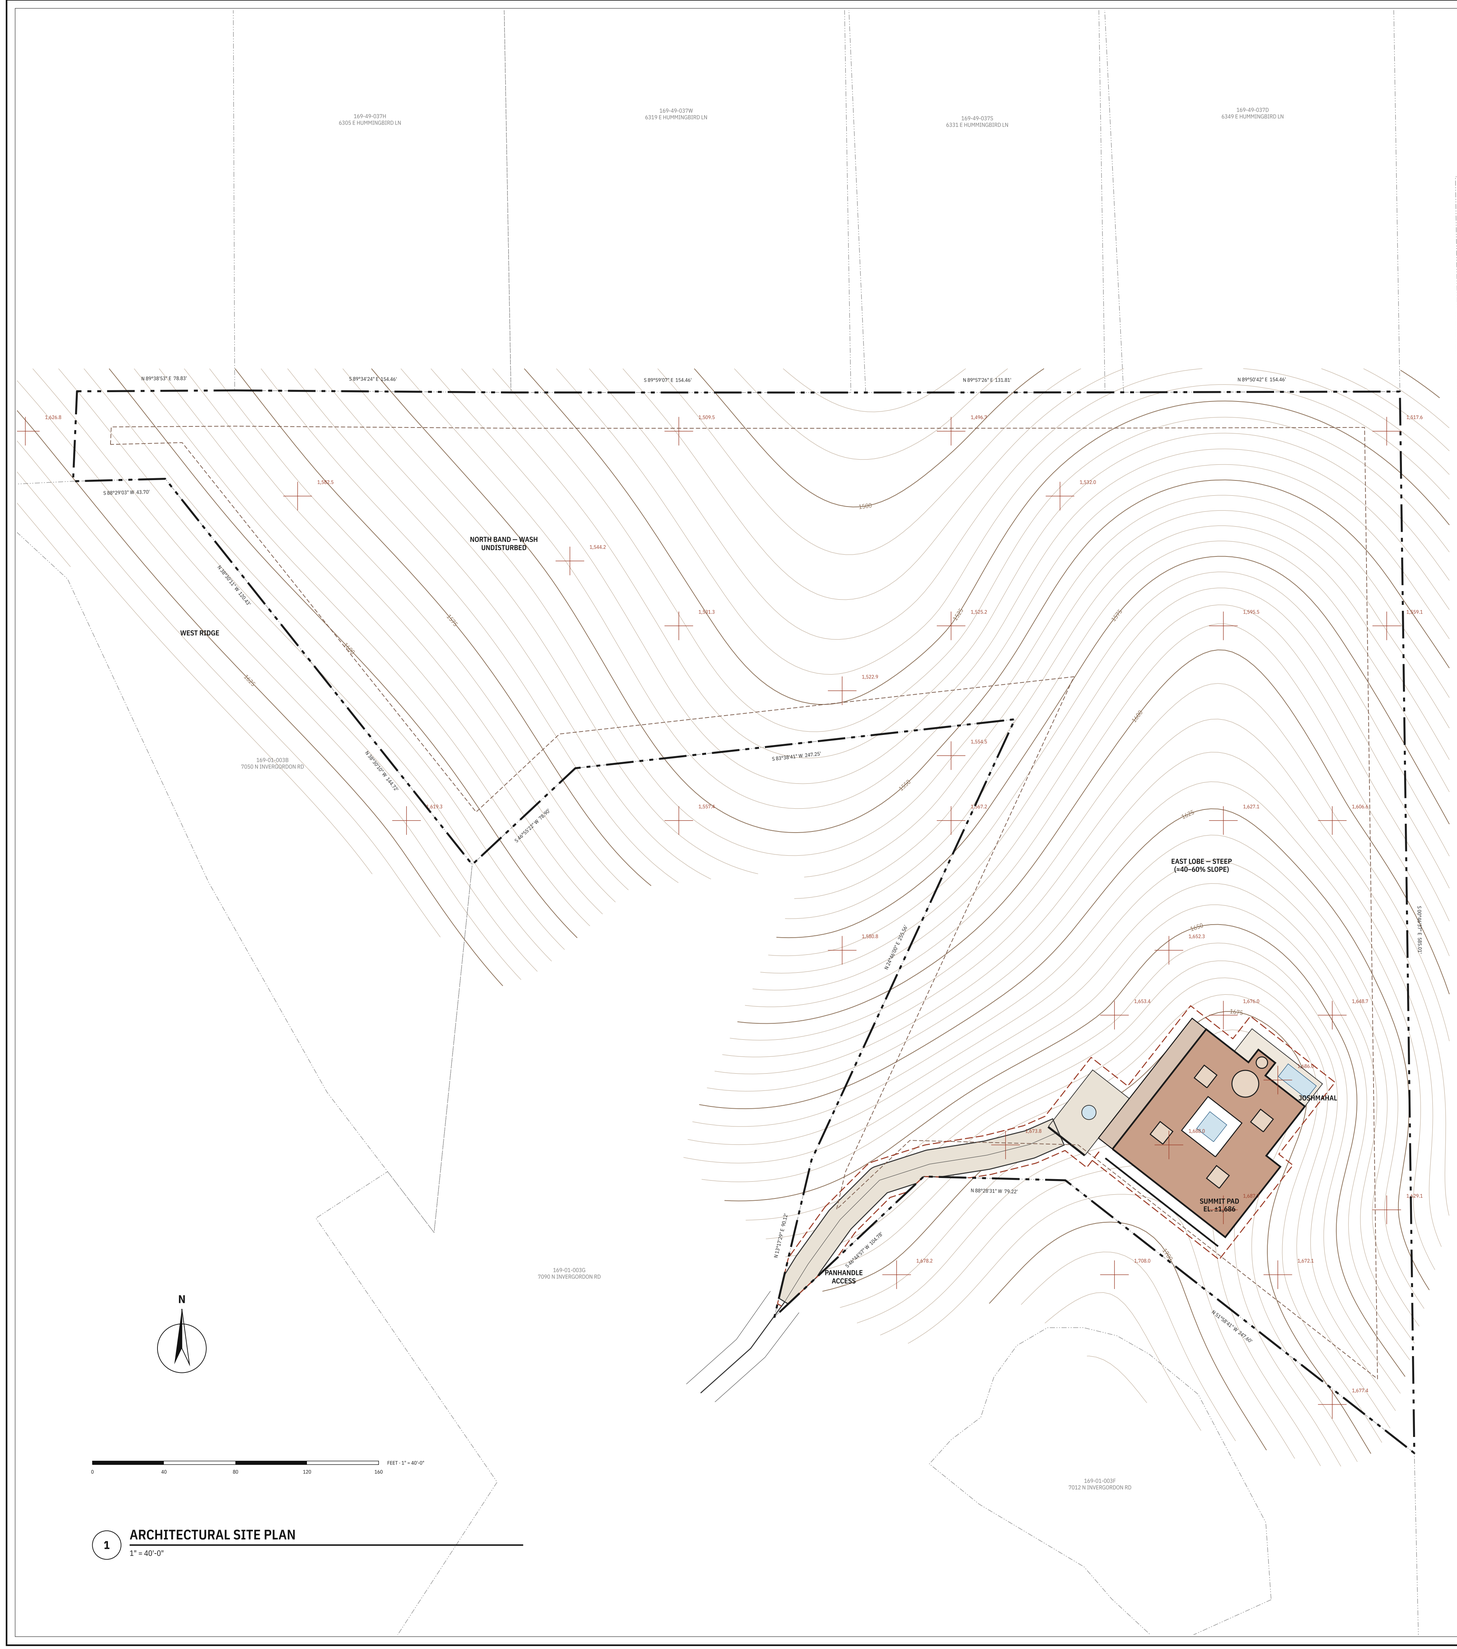

1 ARCHITECTURAL SITE PLAN

1" = 40'-0"

SITE DATA

LOT 225,151 sf (5.17 ac) per Assessor; GIS polygon 219,872 sf (projection tolerance).

GRADE Natural grade within lot EL. 1,488' to 1,701' (+213 ft relief).

SLOPE Average ≈49% (0.0023·I·L/A); summit building site ≈39%.

ACCESS From the private end of Invergordon Rd at the SW panhandle; 16-ft paved drive ≈190 ft to the motor court, ≤ 6% grade.

UTIL. APS electric, water and gas at the property line per listing — confirm locations. No sewer: on-site wastewater system, location by perc test.

FIRE Confirm fire-apparatus access, turnaround and hydrant/fire-flow with the Fire Marshal; residential sprinklers assumed.

LEGEND

Heavy phantom line — property line (Assessor GIS). Thin phantom — adjacent parcels.

Dashed brown — 20'-0" setback (assumed on all lines; verify front/side/rear designations).

Dashed red — limit of disturbance. Brown lines — 5' contours (25' index), interpolated.

+ red — USGS 3DEP LiDAR spot elevations (measured).

Bearings/distances derived from GIS coordinates — not record data.

Landmark VENTURE GROUP

OWNER / DEVELOPER

LANDMARK VENTURE GROUP LLC

Sarvesh Joshi, Managing Partner

Paradise Valley, Arizona

sarvesh@landmarkdigi.com

ARCHITECT OF RECORD

TO BE ENGAGED — ARIZONA-REGISTERED

ARCHITECT (A.R.S. §32-101 et seq.)

NO SEAL

SCHEMATIC STUDY

NOT A REGISTRANT'S DOCUMENT

CONSULTANTS (TO BE ENGAGED)

SURVEY — ALTA / TOPOGRAPHIC

CIVIL — GRADING, DRAINAGE, ON-SITE WASTEWATER

GEOTECHNICAL

STRUCTURAL

MEP / FIRE PROTECTION

LANDSCAPE — NATIVE REVEGETATION

JOSHMAHAL

PRIVATE RESIDENCE

7080 N INVERGORDON ROAD

PARADISE VALLEY, ARIZONA 85253

APN 169-01-003D · 225,151 SF (5.17 AC)

ISSUES / REVISIONS

NO.	DATE	DESCRIPTION
0	10/18/26	SCHEMATIC DESIGN — SD-01


PHASE

SCHEMATIC DESIGN

DATE OCT 18, 2026 PROJECT JM-2610

DRAWN LVG CHECKED —

KEY PLAN

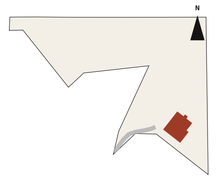

SHEET TITLE

ARCHITECTURAL SITE PLAN

SCALE: 1" = 40'-0"

SHEET

AS-101

3 OF 12


NOT FOR CONSTRUCTION

NOT FOR PERMIT · NOT FOR BIDDING

SCHEMATIC DESIGN — FOR OWNER REVIEW

Schematic study for owner planning. Parcel geometry: Maricopa County Assessor GIS (APN 169-01-003D). Terrain: USGS 3DEP 1-m LiDAR spot elevations (EPQS), interpolated — not a survey. All dimensions, grades, setbacks and code determinations to be verified by an Arizona-registered architect, engineer and land surveyor before design development.

© 2026 Landmark Venture Group LLC · JM-2610 · AS-101

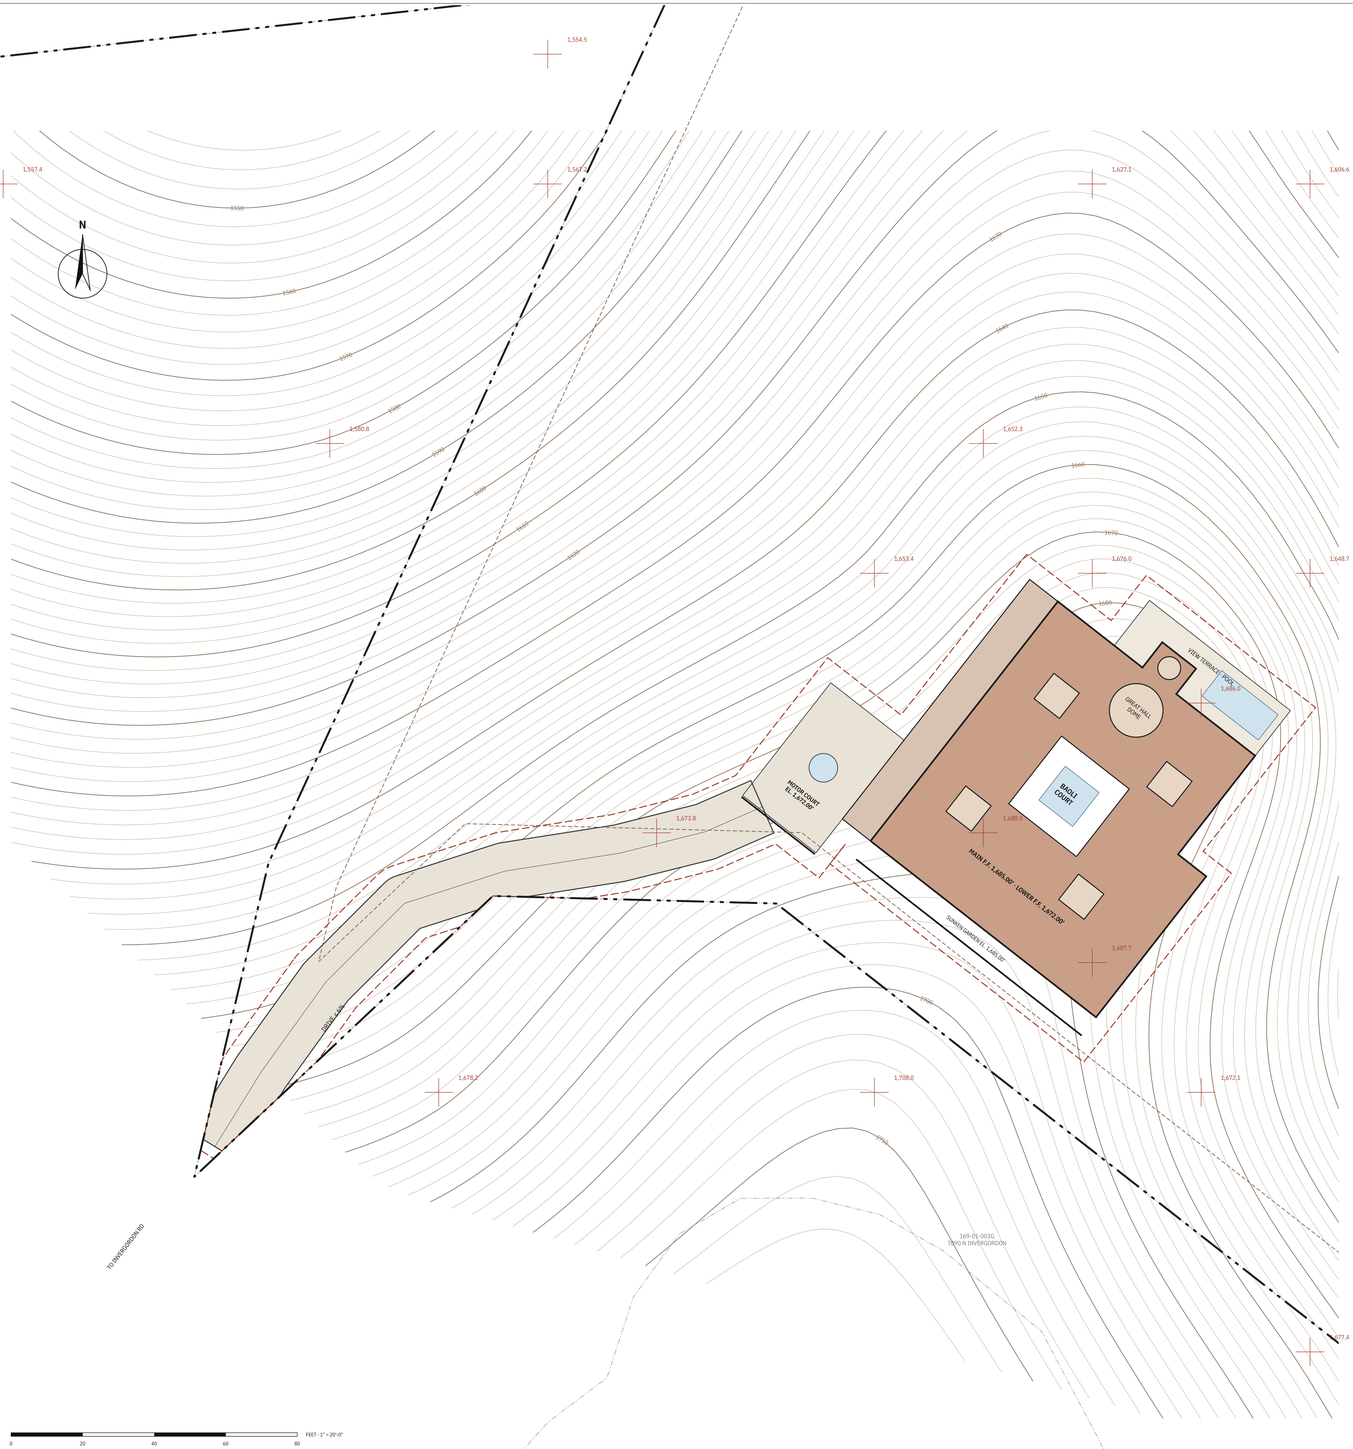

1 ENLARGED SITE PLAN — SUMMIT

1" = 20'-0" · 2' CONTOURS INTERPOLATED FROM LIDAR

LIMIT OF DISTURBANCE

DISTURBANCE	SF
Lower level + garage footprint	7,300
Main level beyond lower	108
Motor court	1,040
View terrace + pool	584
Sunken garden	560
Drive (on site)	2,948
Work zone / overlap (net)	3,388
TOTAL DISTURBED	**15,928**

GRADING & SITE NOTES

1. Main level set at EL. 1,685.00' by cutting ≈5–15 ft into the summit knoll; lower level EL. 1,672.00' is fully below grade except at the motor court.
2. Motor court EL. 1,672.00' — cut on the SE, fill ≤ 5 ft on the NW; tiered retaining ≤ 8'-0" exposed per tier.
3. SW sunken garden EL. 1,685.00' along the primary suite; tiered stone retaining toward the summit (≤ 8'-0" each tier).
4. Drive: 16 ft wide, ≤ 6% grade, from the panhandle at +EL. 1,676' to the motor court.
5. Salvage and replant native cacti and boulders; revegetate all disturbed edges with native Sonoran species.
6. Stormwater: roof drains to cisterns under the motor court; overflow dispersed to natural washes — retention per Town engineer.
7. Rock excavation expected; confirm by geotechnical borings before finalizing floor elevations.

Landmark VENTURE GROUP

OWNER / DEVELOPER

LANDMARK VENTURE GROUP LLC

Sarvesh Joshi, Managing Partner

Paradise Valley, Arizona

sarvesh@landmarkdigi.com

ARCHITECT OF RECORD

TO BE ENGAGED — ARIZONA-REGISTERED

ARCHITECT (A.R.S. §32-101 et seq.)

NO SEAL

SCHEMATIC STUDY

NOT A REGISTRANT'S DOCUMENT

CONSULTANTS (TO BE ENGAGED)

SURVEY — ALTA / TOPOGRAPHIC

CIVIL — GRADING, DRAINAGE, ON-SITE WASTEWATER

GEOTECHNICAL

STRUCTURAL

MEP / FIRE PROTECTION

LANDSCAPE — NATIVE REVEGETATION

JOSHMAHAL

PRIVATE RESIDENCE

7080 N INVERGORDON ROAD

PARADISE VALLEY, ARIZONA 85253

APN 169-01-003D · 225,151 SF (5.17 AC)

ISSUES / REVISIONS

NO.	DATE	DESCRIPTION
0	10/18/26	SCHEMATIC DESIGN — SD-01

PHASE

SCHEMATIC DESIGN


DATE OCT 18, 2026

PROJECT JM-2610

DRAWN LVG

CHECKED —

KEY PLAN

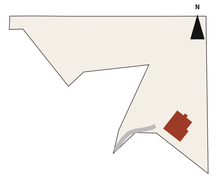

SHEET TITLE

ENLARGED SITE PLAN — SUMMIT

SCALE: 1" = 20'-0"

SHEET

AS-102

4 OF 12


NOT FOR CONSTRUCTION

NOT FOR PERMIT · NOT FOR BIDDING

SCHEMATIC DESIGN — FOR OWNER REVIEW

Schematic study for owner planning. Parcel geometry: Maricopa County Assessor GIS (APN 169-01-003D). Terrain: USGS 3DEP 1-m LiDAR spot elevations (EPQS), interpolated — not a survey. All dimensions, grades, setbacks and code determinations to be verified by an Arizona-registered architect, engineer and land surveyor before design development.

© 2026 Landmark Venture Group LLC · JM-2610 · AS-102

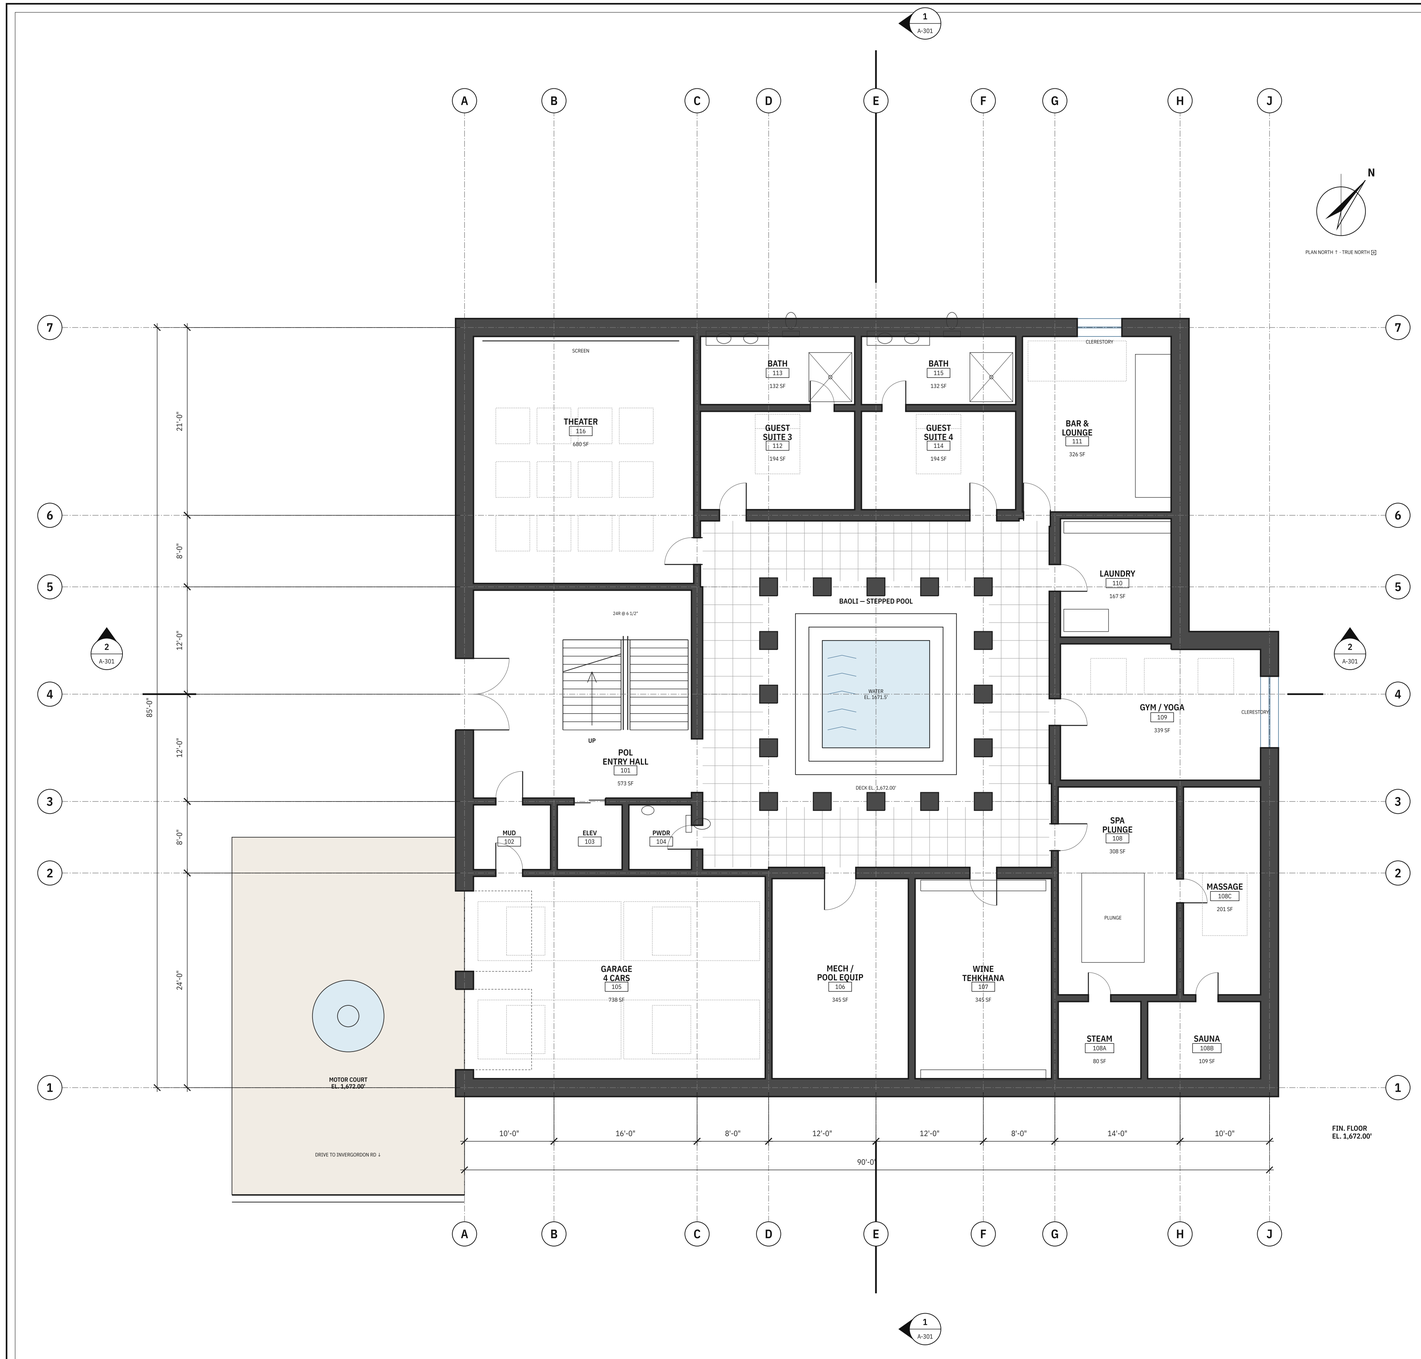

1 LOWER LEVEL FLOOR PLAN

1/8" = 1'-0"

GENERAL NOTES

1. Dimensions are to grid lines / wall centerlines unless noted. Exterior walls 2'-0" (16" conc./CMU + 4" sandstone veneer); interior partitions 9"; gallery walls 15" masonry.
2. Gallery around the baoli court is enclosed and conditioned; arched openings to the court are glazed below a jaali guard at 42" A.F.F.
3. All bedrooms have emergency escape openings: lower-level guest suites open to the baoli court, which is open to sky.
4. Fixtures and furniture are shown for scale only.
5. Elevator and stair connect both levels; roof access by hatch (AV closet).

ROOM AREAS

NO.	ROOM	NET SF
101	POL ENTRY HALL	573
102	MUD	63
103	ELEV	53
104	PWDR	53
105	GARAGE 4 CARS	738
106	MECH / POOL EQUIP	345
107	WINE TEHKHANA	345
108	SPA PLUNGE	308
108A	STEAM	80
108B	SAUNA	109
108C	MASSAGE	201
109	GYM / YOGA	339
110	LAUNDRY	167
111	BAR & LOUNGE	326
112	GUEST SUITE 3	194
113	BATH	132
114	GUEST SUITE 4	194
115	BATH	132
116	THEATER	680
—	GALLERY (CONDITIONED)	850
	GROSS (INCL. GARAGE)	**6,724**

WALL LEGEND

Solid dark — load-bearing masonry / concrete walls (cut).

Grey squares — 2'-0" stone piers at the baoli court.

Blue triple line — glazing; projecting outline — carved jharokha balcony.

Dashed — overhead / below (dome, arches, garage doors, open-to-below).

Landmark VENTURE GROUP

OWNER / DEVELOPER

LANDMARK VENTURE GROUP LLC

Sarvesh Joshi, Managing Partner

Paradise Valley, Arizona

sarvesh@landmarkdigi.com

ARCHITECT OF RECORD

TO BE ENGAGED — ARIZONA-REGISTERED

ARCHITECT (A.R.S. §32-101 et seq.)

NO SEAL

SCHEMATIC STUDY

NOT A REGISTRANT'S DOCUMENT

CONSULTANTS (TO BE ENGAGED)

SURVEY — ALTA / TOPOGRAPHIC

CIVIL — GRADING, DRAINAGE, ON-SITE WASTEWATER

GEOTECHNICAL

STRUCTURAL

MEP / FSRE PROTECTION

LANDSCAPE — NATIVE REVEGETATION

JOSHMAHAL

PRIVATE RESIDENCE

7080 N INVERGORDON ROAD

PARADISE VALLEY, ARIZONA 85253

APN 169-01-003D · 225,151 SF (5.17 AC)

ISSUES / REVISIONS

NO.	DATE	DESCRIPTION
0	10/18/26	SCHEMATIC DESIGN — SD-01

PHASE

SCHEMATIC DESIGN


DATE OCT 18, 2026

PROJECT JM-2610

DRAWN LVG

CHECKED —

KEY PLAN

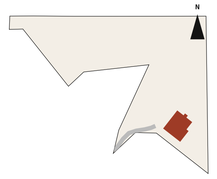

SHEET TITLE

LOWER LEVEL FLOOR PLAN

SCALE: 1/8" = 1'-0"

SHEET

A-101

5 OF 12


NOT FOR CONSTRUCTION

NOT FOR PERMIT - NOT FOR BIDDING

SCHEMATIC DESIGN — FOR OWNER REVIEW

Schematic study for owner planning. Parcel geometry: Maricopa County Assessor GIS (APN 169-01-003D). Terrain: USGS 3DEP 1-m LiDAR spot elevations (EPQS), interpolated — not a survey. All dimensions, grades, setbacks and code determinations to be verified by an Arizona-registered architect, engineer and land surveyor before design development.

© 2026 Landmark Venture Group LLC · JM-2610 · A-101

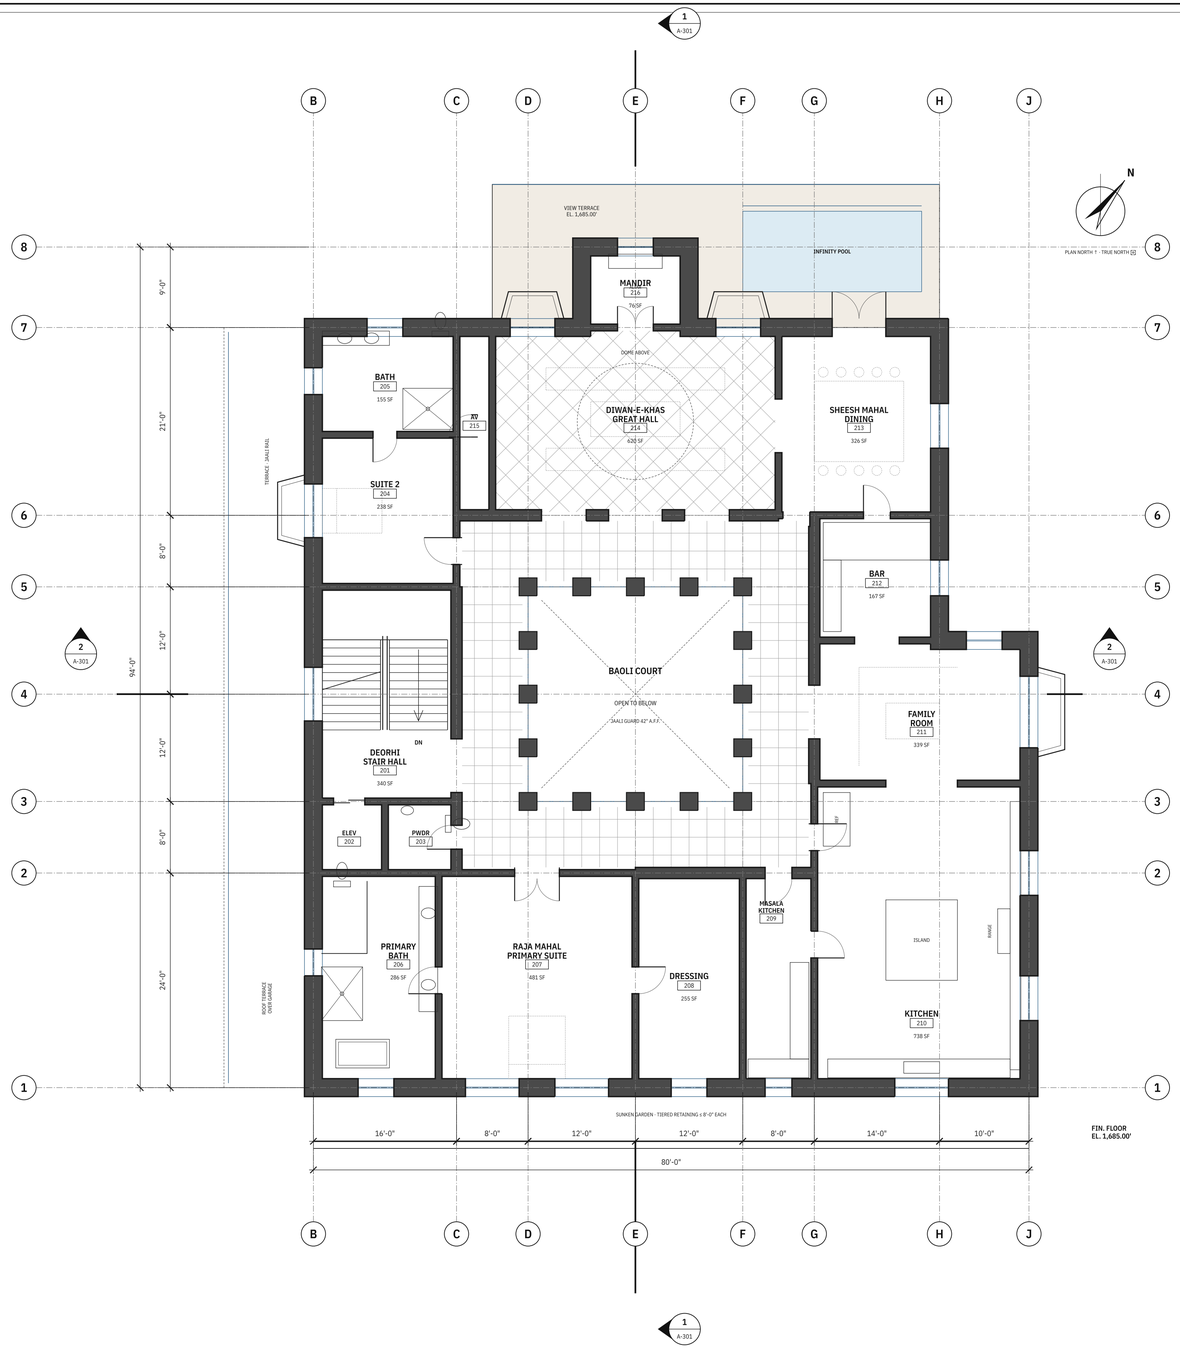

1 MAIN LEVEL FLOOR PLAN

1/8" = 1'-0"

GENERAL NOTES

1. Dimensions are to grid lines / wall centerlines unless noted. Exterior walls 2'-0" (16" conc./CMU + 4" sandstone veneer); interior partitions 9"; gallery walls 15" masonry.
2. Gallery around the baoli court is enclosed and conditioned; arched openings to the court are glazed below a jaali guard at 42" A.F.F.
3. All bedrooms have emergency escape openings: lower-level guest suites open to the baoli court, which is open to sky.
4. Fixtures and furniture are shown for scale only.
5. Elevator and stair connect both levels; roof access by hatch (AV closet).

ROOM AREAS

NO.	ROOM	NET SF
201	DEORHI STAIR HALL	340
202	ELEV	48
203	PWDR	53
204	SUITE 2	238
205	BATH	155
206	PRIMARY BATH	286
207	RAJA MAHAL PRIMARY SUITE	481
208	DRESSING	255
209	MASALA KITCHEN	164
210	KITCHEN	738
211	FAMILY ROOM	339
212	BAR	167
213	SHEESH MAHAL DINING	326
214	DIWAN-E-KHAS GREAT HALL	620
215	AV	64
216	MANDIR	76
—	GALLERY (CONDITIONED)	850
	GROSS	**5,982**

WALL LEGEND

Solid dark — load-bearing masonry / concrete walls (cut).

Grey squares — 2'-0" stone piers at the baoli court.

Blue triple line — glazing; projecting outline — carved jharokha balcony.

Dashed — overhead / below (dome, arches, garage doors, open-to-below).

Landmark VENTURE GROUP

OWNER / DEVELOPER

LANDMARK VENTURE GROUP LLC

Sarvesh Joshi, Managing Partner

Paradise Valley, Arizona

sarvesh@landmarkdigi.com

ARCHITECT OF RECORD

TO BE ENGAGED — ARIZONA-REGISTERED

ARCHITECT (A.R.S. §32-101 et seq.)

NO SEAL

SCHEMATIC STUDY

NOT A REGISTRANT'S DOCUMENT

CONSULTANTS (TO BE ENGAGED)

SURVEY — ALTA / TOPOGRAPHIC

CIVIL — GRADING, DRAINAGE, ON-SITE WASTEWATER

GEOTECHNICAL

STRUCTURAL

MEP / FIRE PROTECTION

LANDSCAPE — NATIVE REVEGETATION

JOSHMAHAL

PRIVATE RESIDENCE

7080 N INVERGORDON ROAD

PARADISE VALLEY, ARIZONA 85253

APN 169-01-003D · 225,151 SF (5.17 AC)

ISSUES / REVISIONS

NO.	DATE	DESCRIPTION
0	10/18/26	SCHEMATIC DESIGN — SD-01

PHASE

SCHEMATIC DESIGN


DATE OCT 18, 2026

PROJECT JM-2610

DRAWN LVG

CHECKED —

KEY PLAN

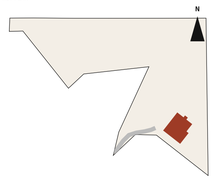

SHEET TITLE

MAIN LEVEL FLOOR PLAN

SCALE: 1/8" = 1'-0"

SHEET

A-102

6 OF 12


NOT FOR CONSTRUCTION

NOT FOR PERMIT · NOT FOR BIDDING

SCHEMATIC DESIGN — FOR OWNER REVIEW

Schematic study for owner planning. Parcel geometry: Maricopa County Assessor GIS (APN 169-01-003D). Terrain: USGS 3DEP 1-m LiDAR spot elevations (EPQS), interpolated — not a survey. All dimensions, grades, setbacks and code determinations to be verified by an Arizona-registered architect, engineer and land surveyor before design development.

© 2026 Landmark Venture Group LLC · JM-2610 · A-102

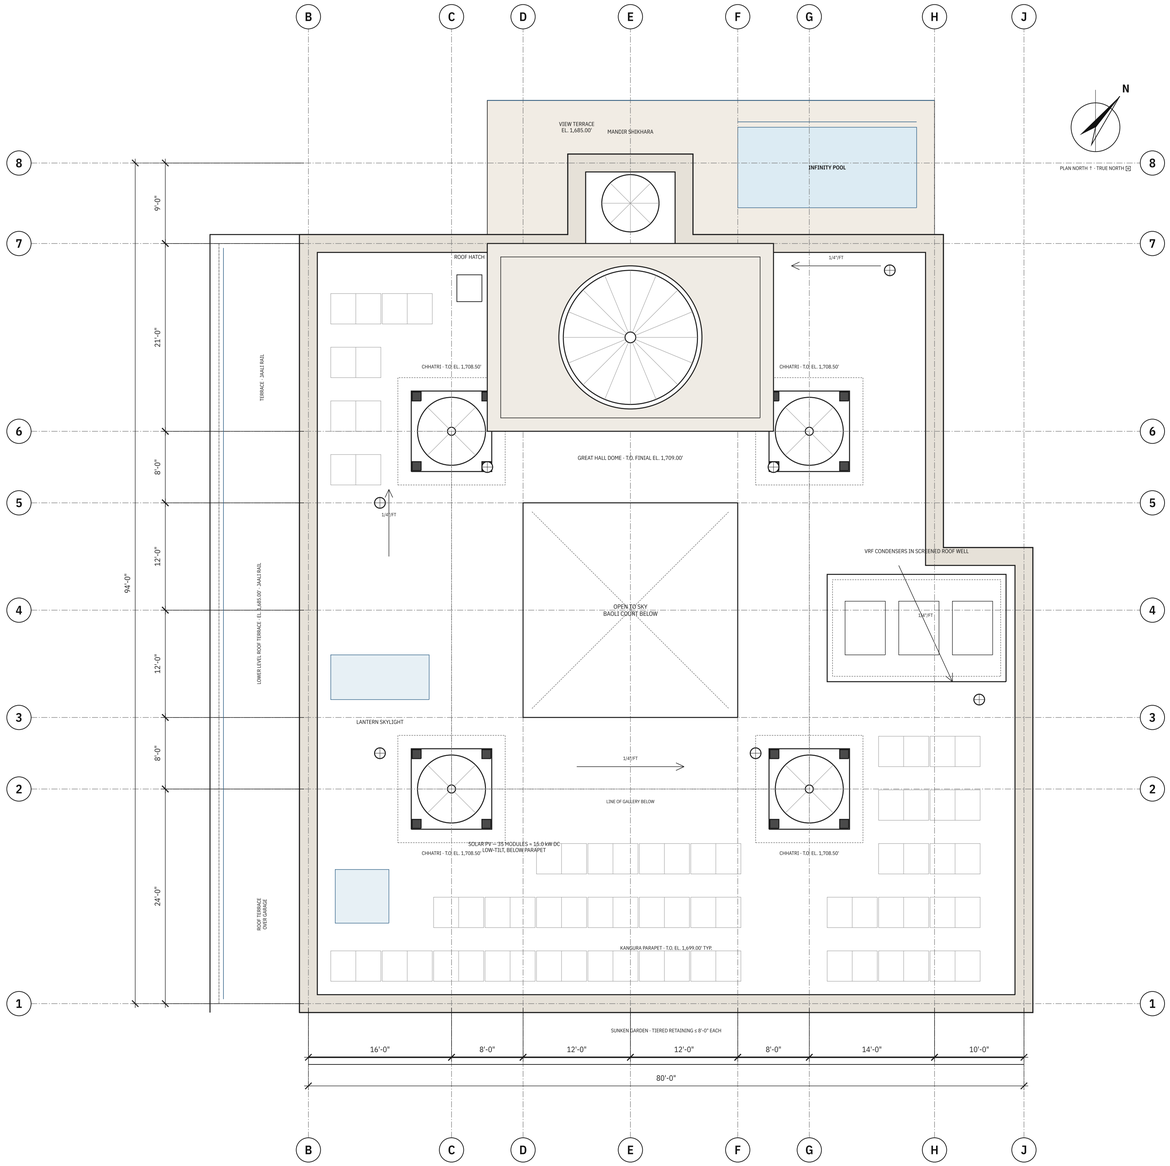

1 ROOF PLAN

1/8" = 1'-0"

ROOF NOTES

1. Roof: 8" concrete deck, tapered polyiso R-30 min. at 1/4"/ft to internal drains, white TPO/PVC membrane (SRI ≥ 82) concealed behind the kangura parapet.
2. Solar PV: 35 modules = 15.0 kW DC, low-tilt racking kept below the parapet so nothing shows from off-site. Final count by PV designer.
3. Drains connect to cisterns under the motor court; overflow scuppers through the parapet with stone spouts.
4. VRF condensing units sit in a recessed, screened roof well over the family room, below the parapet line.
5. Chhatris and dome: carved sandstone over galvanized steel frames; see A-501. No roof-mounted element exceeds the 24-ft plane — see G-002.
6. Rooftop is a usable terrace between the chhatris (guard = parapet, 42" min. above deck).

ROOF ELEVATIONS (NAVD88)

ROOF ELEMENT	ELEVATION
T.O. PARAPET (KANGURA)	1,699.00'
ROOF DECK	1,698.00'
GREAT HALL PARAPET	1,702.50'
DOME DRUM	1,702.50'
DOME FINIAL	1,709.00'
CHHATRI FINIAL	1,708.50'
MANDIR SHIKHARA	1,703.60'

Landmark VENTURE GROUP

OWNER / DEVELOPER

LANDMARK VENTURE GROUP LLC

Sarvesh Joshi, Managing Partner

Paradise Valley, Arizona

sarvesh@landmarkdigi.com

ARCHITECT OF RECORD

TO BE ENGAGED — ARIZONA-REGISTERED

ARCHITECT (A.R.S. §32-101 et seq.)

NO SEAL

SCHEMATIC STUDY

NOT A REGISTRANT'S DOCUMENT

CONSULTANTS (TO BE ENGAGED)

SURVEY — ALTA / TOPOGRAPHIC

CIVIL — GRADING, DRAINAGE, ON-SITE WASTEWATER

GEOTECHNICAL

STRUCTURAL

MEP / FIRE PROTECTION

LANDSCAPE — NATIVE REVEGETATION

JOSHMAHAL

PRIVATE RESIDENCE

7080 N INVERGORDON ROAD

PARADISE VALLEY, ARIZONA 85253

APN 169-01-003D · 225,151 SF (5.17 AC)

ISSUES / REVISIONS

NO.	DATE	DESCRIPTION
0	10/18/26	SCHEMATIC DESIGN — SD-01

PHASE

SCHEMATIC DESIGN


DATE OCT 18, 2026

PROJECT JM-2610

DRAWN LVG

CHECKED —

KEY PLAN

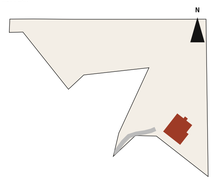

SHEET TITLE

ROOF PLAN

SCALE: 1/8" = 1'-0"

SHEET

A-103

7 OF 12


NOT FOR CONSTRUCTION

NOT FOR PERMIT · NOT FOR BIDDING

SCHEMATIC DESIGN — FOR OWNER REVIEW


Schematic study for owner planning. Parcel geometry: Maricopa County Assessor GIS (APN 169-01-003D). Terrain: USGS 3DEP 1-m LiDAR spot elevations (EPQS), interpolated — not a survey. All dimensions, grades, setbacks and code determinations to be verified by an Arizona-registered architect, engineer and land surveyor before design development.

© 2026 Landmark Venture Group LLC · JM-2610 · A-103

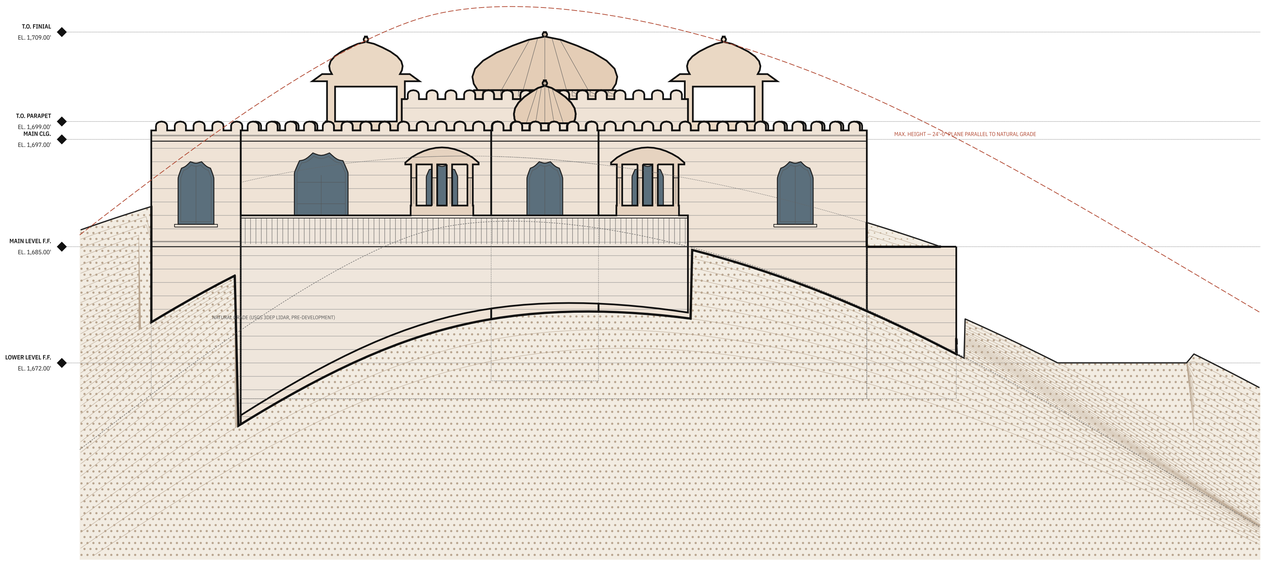

1 NORTHEAST ELEVATION (VIEW SIDE)

1/8" = 1'-0"

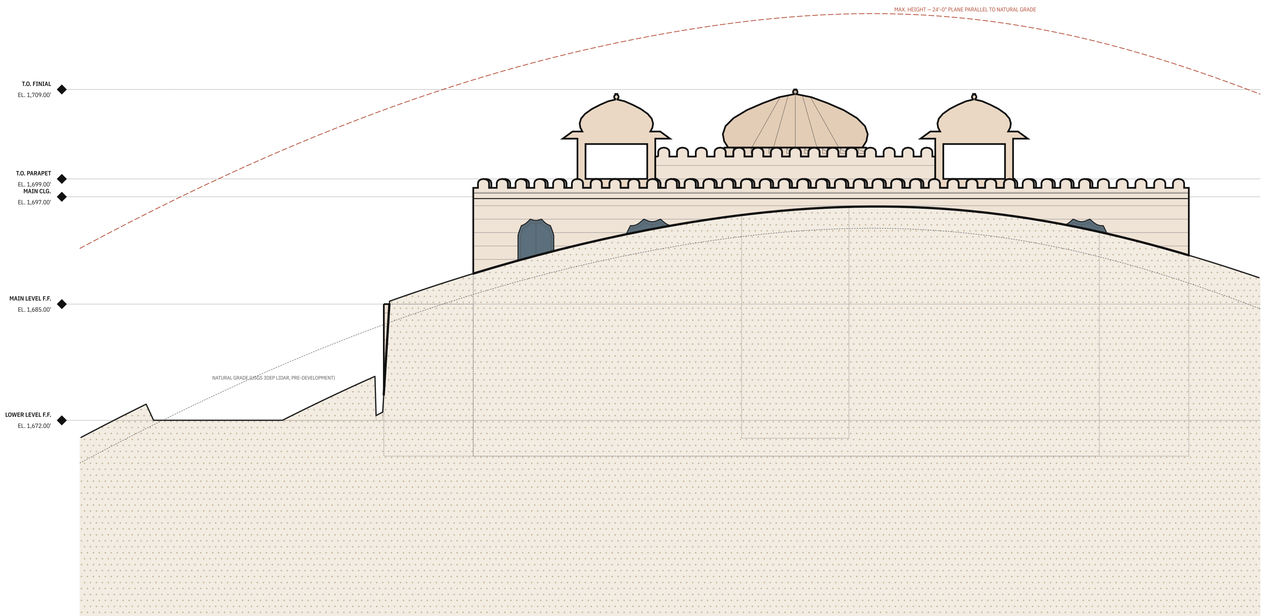

2 SOUTHWEST ELEVATION (ARRIVAL SIDE)

1/8" = 1'-0"

EXTERIOR MATERIALS

- **A** Rose-red sandstone ashlar, chisel finish, 18" coursing — LRV ≤ 32 (sample board to Hillside Committee).
- **B** Deep ochre sandstone — chajja cornices, string courses, chhatri and jharokha carving — LRV ≤ 35.
- **C** Kangura parapet: carved stone merlons on stone coping.
- **D** Windows: low-reflectance low-E glass in bronze-finish frames, set deep in cusped stone arches.
- **E** Gate and garage doors: smoked teak with hand-forged brass studs.
- **F** Dome and finials: carved stone segments on steel frame; patinated bronze kalash, matte.
- **G** Jaali: 2" pierced sandstone screens at jharokhas and terrace guards.

NOTES

1. Natural grade (dashed) and the 24'-0" height plane (red dashed) are drawn at the façade plane from the LiDAR surface; landform beyond is shaded.
2. Every roof element was checked against the plane on a 1-ft grid — see G-002 for margins.
3. Building portions below grade are shown dashed.

Landmark VENTURE GROUP

OWNER / DEVELOPER

LANDMARK VENTURE GROUP LLC

Sarvesh Joshi, Managing Partner

Paradise Valley, Arizona

sarvesh@landmarkdigi.com

ARCHITECT OF RECORD

TO BE ENGAGED — ARIZONA-REGISTERED

ARCHITECT (A.R.S. §32-101 et seq.)

NO SEAL

SCHEMATIC STUDY

NOT A REGISTRANT'S DOCUMENT

CONSULTANTS (TO BE ENGAGED)

SURVEY — ALTA / TOPOGRAPHIC

CIVIL — GRADING, DRAINAGE, ON-SITE WASTEWATER

GEOTECHNICAL

STRUCTURAL

MEP / FIRE PROTECTION

LANDSCAPE — NATIVE REVEGETATION

JOSHMAHAL

PRIVATE RESIDENCE

7080 N INVERGORDON ROAD

PARADISE VALLEY, ARIZONA 85253

APN 169-01-003D · 225,151 SF (5.17 AC)

ISSUES / REVISIONS

NO.	DATE	DESCRIPTION
0	10/18/26	SCHEMATIC DESIGN — SD-01


PHASE

SCHEMATIC DESIGN

DATE OCT 18, 2026 PROJECT JM-2610

DRAWN LVG CHECKED —

KEY PLAN

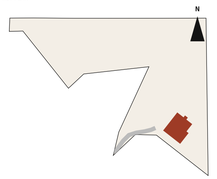

SHEET TITLE

EXTERIOR ELEVATIONS

SCALE: 1/8" = 1'-0"

SHEET

A-201

8 OF 12


NOT FOR CONSTRUCTION

NOT FOR PERMIT · NOT FOR BIDDING

SCHEMATIC DESIGN — FOR OWNER REVIEW


Schematic study for owner planning. Parcel geometry: Maricopa County Assessor GIS (APN 169-01-003D). Terrain: USGS 3DEP 1-m LiDAR spot elevations (EPQS), interpolated — not a survey. All dimensions, grades, setbacks and code determinations to be verified by an Arizona-registered architect, engineer and land surveyor before design development.

© 2026 Landmark Venture Group LLC · JM-2610 · A-201

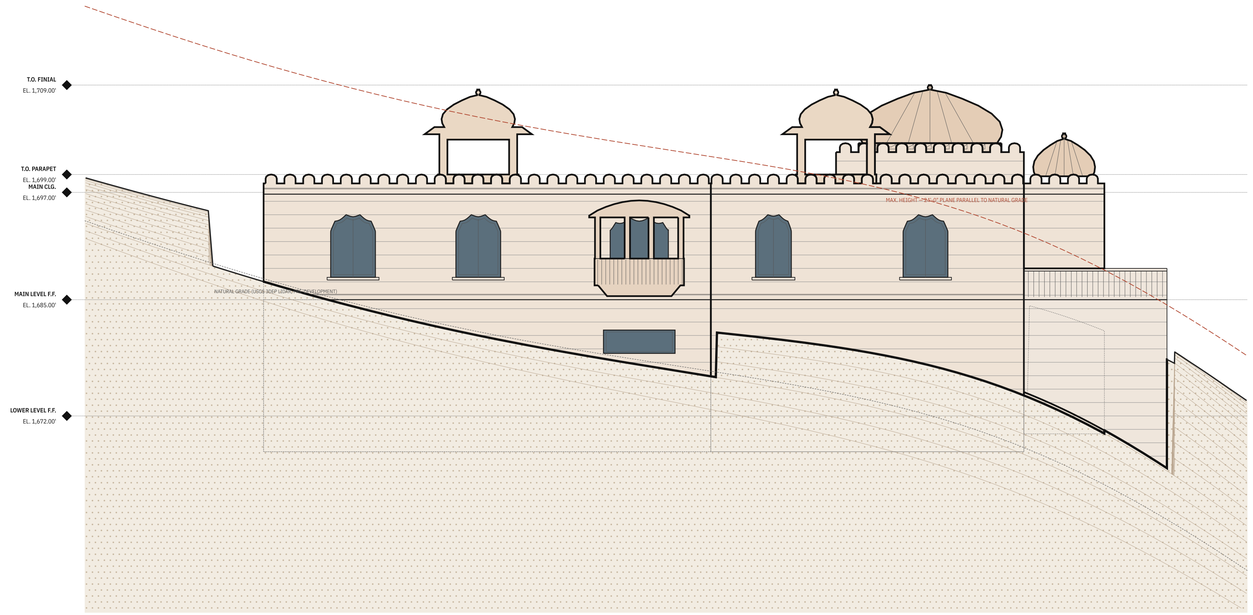

1 SOUTHEAST ELEVATION

1/8" = 1'-0"

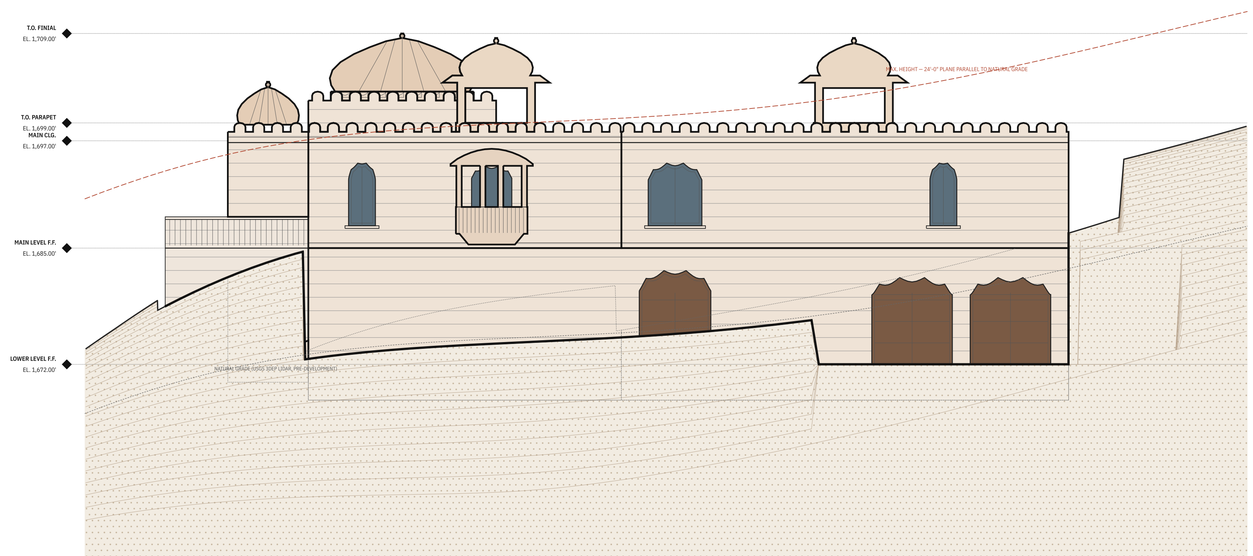

2 NORTHWEST ELEVATION (MOTOR COURT)

1/8" = 1'-0"

EXTERIOR MATERIALS

- **A** Rose-red sandstone ashlar, chisel finish, 18" coursing — LRV ≤ 32 (sample board to Hillside Committee).
- **B** Deep ochre sandstone — chajja cornices, string courses, chhatri and jharokha carving — LRV ≤ 35.
- **C** Kangura parapet: carved stone merlons on stone coping.
- **D** Windows: low-reflectance low-E glass in bronze-finish frames, set deep in cusped stone arches.
- **E** Gate and garage doors: smoked teak with hand-forged brass studs.
- **F** Dome and finials: carved stone segments on steel frame; patinated bronze kalash, matte.
- **G** Jaali: 2" pierced sandstone screens at jharokhas and terrace guards.

NOTES

1. Natural grade (dashed) and the 24'-0" height plane (red dashed) are drawn at the façade plane from the LiDAR surface; landform beyond is shaded.
2. Every roof element was checked against the plane on a 1-ft grid — see G-002 for margins.
3. Building portions below grade are shown dashed.

Landmark VENTURE GROUP

OWNER / DEVELOPER

LANDMARK VENTURE GROUP LLC

Sarvesh Joshi, Managing Partner

Paradise Valley, Arizona

sarvesh@landmarkdigi.com

ARCHITECT OF RECORD

TO BE ENGAGED — ARIZONA-REGISTERED

ARCHITECT (A.R.S. §32-101 et seq.)

NO SEAL

SCHEMATIC STUDY

NOT A REGISTRANT'S DOCUMENT

CONSULTANTS (TO BE ENGAGED)

SURVEY — ALTA / TOPOGRAPHIC

CIVIL — GRADING, DRAINAGE, ON-SITE WASTEWATER

GEOTECHNICAL

STRUCTURAL

MEP / FIRE PROTECTION

LANDSCAPE — NATIVE REVEGETATION

JOSHMAHAL

PRIVATE RESIDENCE

7080 N INVERGORDON ROAD

PARADISE VALLEY, ARIZONA 85253

APN 169-01-003D · 225,151 SF (5.17 AC)

ISSUES / REVISIONS

NO.	DATE	DESCRIPTION
0	10/18/26	SCHEMATIC DESIGN — SD-01

PHASE

SCHEMATIC DESIGN


DATE OCT 18, 2026

PROJECT JM-2610

DRAWN LVG

CHECKED —

KEY PLAN

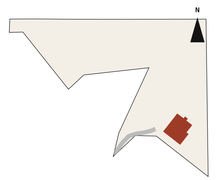

SHEET TITLE

EXTERIOR ELEVATIONS

SCALE: 1/8" = 1'-0"

SHEET

A-202


9 OF 12

NOT FOR CONSTRUCTION

NOT FOR PERMIT · NOT FOR BIDDING


SCHEMATIC DESIGN — FOR OWNER REVIEW

© 2026 Landmark Venture Group LLC · JM-2610 · A-202

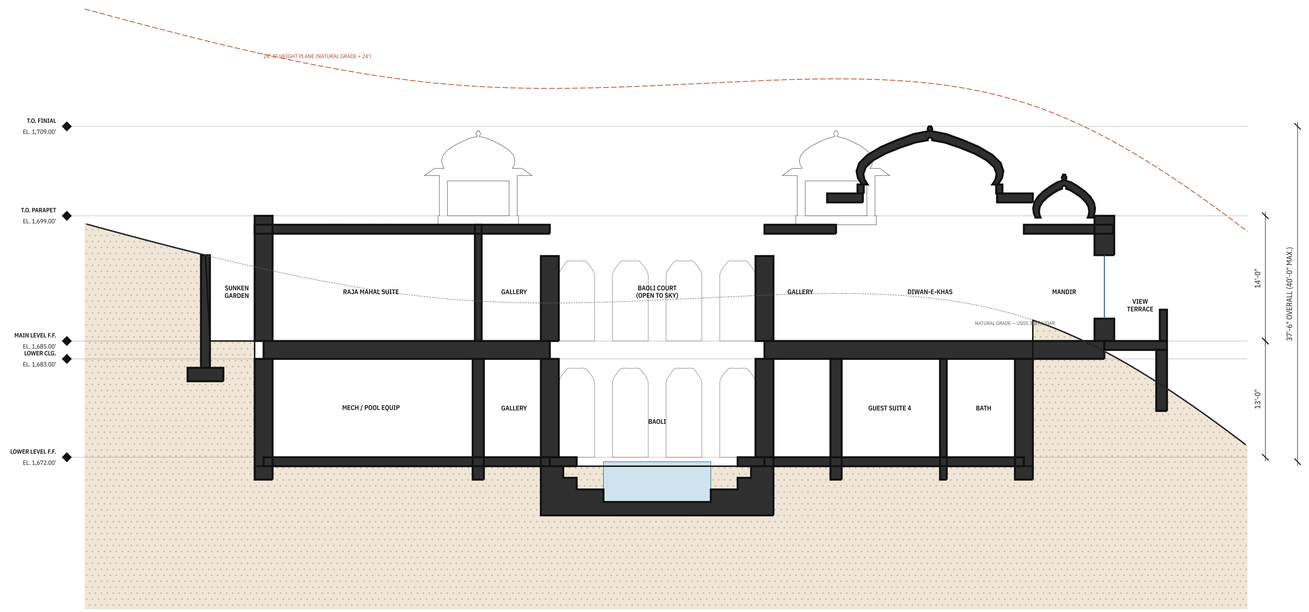

1 SECTION 1 — LOOKING NW

1/8" = 1'-0"

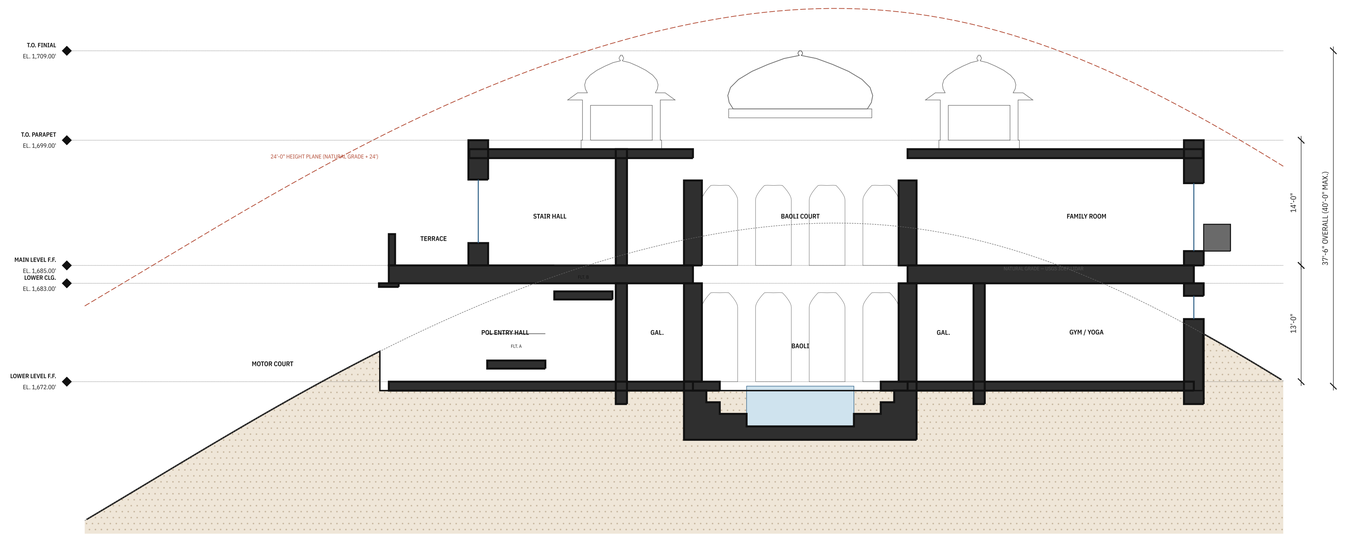

2 SECTION 2 — LOOKING NE

1/8" = 1'-0"

SECTION NOTES

1. Lower level is cut into the summit rock; walls below grade are 16" reinforced concrete with waterproofing and drainage composite (see A-501, detail 5).
2. The baoli court is open to the sky from the stepped pool (water EL. 1,671.50') to the roof, bringing daylight and egress to the lower level.
3. Overall height 37'-6" from the lowest built point (court water edge EL. 1,671.50') to the dome finial (EL. 1,709.00') — 40'-0" max.
4. Floor-to-floor 13'-0"; main level ceilings 12'-0", great hall rises into the dome.

Landmark VENTURE GROUP

OWNER / DEVELOPER

LANDMARK VENTURE GROUP LLC

Sarvesh Joshi, Managing Partner

Paradise Valley, Arizona

sarvesh@landmarkdigi.com

ARCHITECT OF RECORD

TO BE ENGAGED — ARIZONA-REGISTERED

ARCHITECT (A.R.S. §32-101 et seq.)

NO SEAL

SCHEMATIC STUDY

NOT A REGISTRANT'S DOCUMENT

CONSULTANTS (TO BE ENGAGED)

SURVEY — ALTA / TOPOGRAPHIC

CIVIL — GRADING, DRAINAGE, ON-SITE WASTEWATER

GEOTECHNICAL

STRUCTURAL

MEP / FIRE PROTECTION

LANDSCAPE — NATIVE REVEGETATION

JOSHMAHAL

PRIVATE RESIDENCE

7080 N INVERGORDON ROAD

PARADISE VALLEY, ARIZONA 85253

APN 169-01-003D · 225,151 SF (5.17 AC)

ISSUES / REVISIONS

NO.	DATE	DESCRIPTION
0	10/18/26	SCHEMATIC DESIGN — SD-01


PHASE

SCHEMATIC DESIGN

DATE OCT 18, 2026 PROJECT JM-2610

DRAWN LVG CHECKED —

KEY PLAN

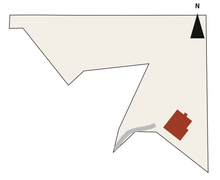

SHEET TITLE

BUILDING SECTIONS

SCALE: 1/8" = 1'-0"

SHEET

A-301

10 OF 12


NOT FOR CONSTRUCTION

NOT FOR PERMIT · NOT FOR BIDDING

SCHEMATIC DESIGN — FOR OWNER REVIEW


Schematic study for owner planning. Parcel geometry: Maricopa County Assessor GIS (APN 169-01-003D). Terrain: USGS 3DEP 1-m LiDAR spot elevations (EPQS), interpolated — not a survey. All dimensions, grades, setbacks and code determinations to be verified by an Arizona-registered architect, engineer and land surveyor before design development.

© 2026 Landmark Venture Group LLC · JM-2610 · A-301

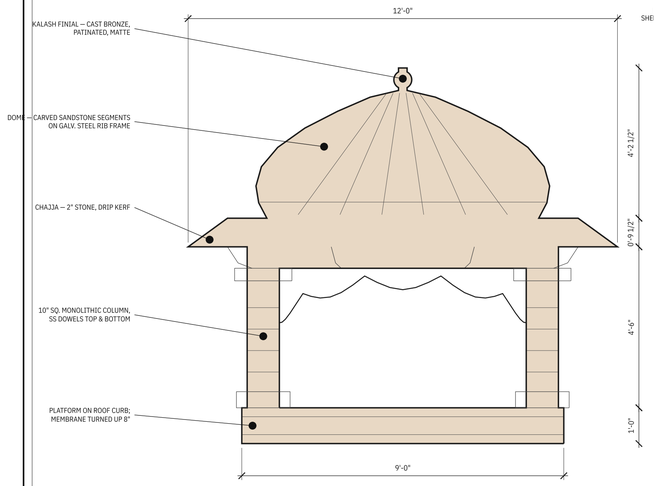


1 CHHATRI — ELEVATION

1/2" = 1'-0"

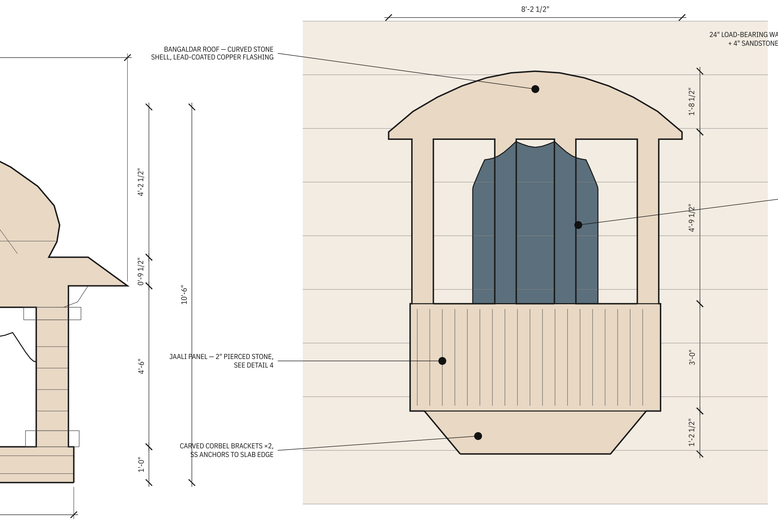


2 JHAROKHA — ELEVATION

1/2" = 1'-0"

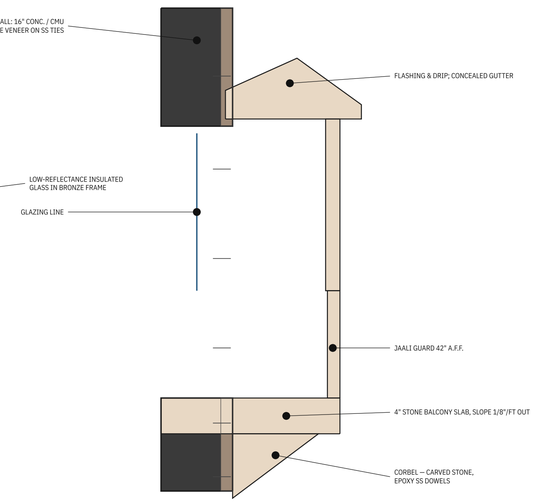


3 JHAROKHA — SECTION

1/2" = 1'-0"

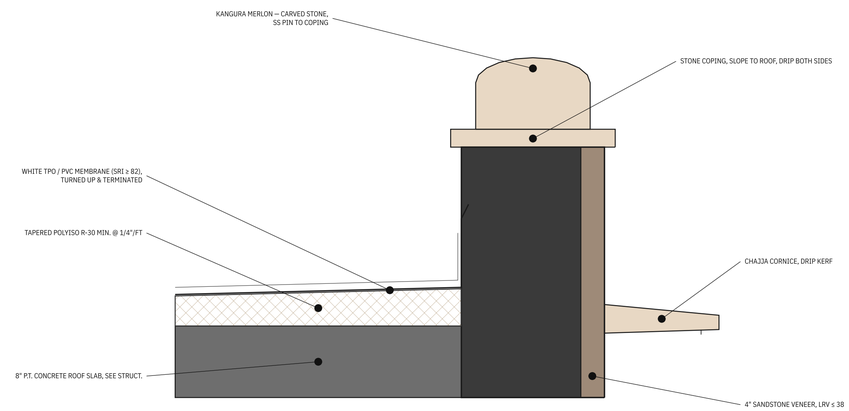

4 KANGURA PARAPET & CHAJJA


1" = 1'-0"

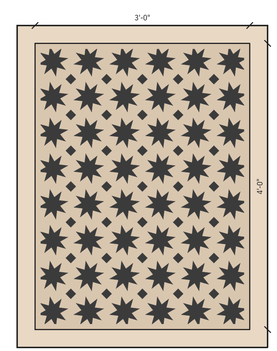

2" PIERCED SANDSTONE · 6" MODULE 8-POINT STAR LATTICE · ±45% OPEN AREA

5 JAALI SCREEN PANEL

1" = 1'-0"

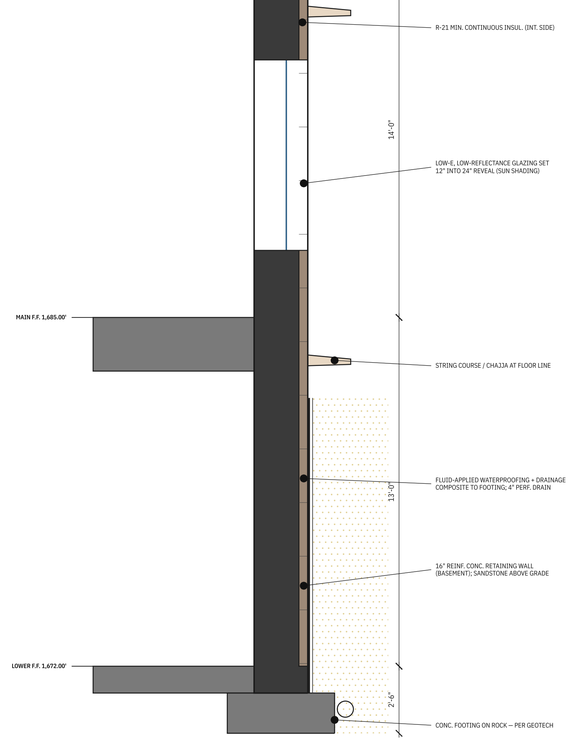

6 TYPICAL EXTERIOR WALL SECTION

3/8" = 1'-0"

Landmark VENTURE GROUP

OWNER / DEVELOPER

LANDMARK VENTURE GROUP LLC

Sarvesh Joshi, Managing Partner

Paradise Valley, Arizona

sarvesh@landmarkdigi.com

ARCHITECT OF RECORD

TO BE ENGAGED — ARIZONA-REGISTERED

ARCHITECT (A.R.S. §32-101 et seq.)

NO SEAL

SCHEMATIC STUDY

NOT A REGISTRANT'S DOCUMENT

CONSULTANTS (TO BE ENGAGED)

SURVEY — ALTA / TOPOGRAPHIC

CIVIL — GRADING, DRAINAGE, ON-SITE WASTEWATER

GEOTECHNICAL

STRUCTURAL

MEP / FIRE PROTECTION

LANDSCAPE — NATIVE REVEGETATION

JOSHMAHAL

PRIVATE RESIDENCE

7080 N INVERGORDON ROAD

PARADISE VALLEY, ARIZONA 85253

APN 169-01-003D · 225,151 SF (5.17 AC)

ISSUES / REVISIONS

NO.	DATE	DESCRIPTION
0	10/18/26	SCHEMATIC DESIGN — SD-01


PHASE

SCHEMATIC DESIGN

DATE OCT 18, 2026 PROJECT JM-2610

DRAWN LVG CHECKED —

KEY PLAN

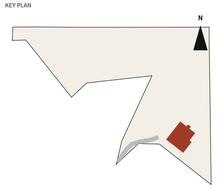

SHEET TITLE

EXTERIOR DETAILS

SCALE: AS NOTED

SHEET

A-501

11 OF 12

NOT FOR CONSTRUCTION

NOT FOR PERMIT · NOT FOR BIDDING

SCHEMATIC DESIGN — FOR OWNER REVIEW

Schematic study for owner planning. Parcel geometry: Maricopa County Assessor GIS (APN 169-01-0030). Terrain: USGS 3DEP 1-m LiDAR spot elevations (EPQS), interpolated — not a survey. All dimensions, grades, setbacks and code determinations to be verified by an Arizona-registered architect, engineer and land surveyor before design development.

© 2026 Landmark Venture Group LLC · JM-2610 · A-501

ROOM FINISH SCHEDULE

NO.	ROOM	FLOOR	WALLS	CLG.	HT.	NET SF
101	POL ENTRY HALL	F3	W2	C2	11'-0"	573
102	MUD	F3	W7	C4	10'-0"	63
103	ELEV	—	—	—	—	53
104	PWDR	F1	W1	C1	9'-0"	53
105	GARAGE 4 CARS	F5	W7	C4	10'-0"	738
106	MECH / POOL EQUIP	F5	W7	C4	11'-0"	345
107	WINE TEHKHANA	F3	W4	C2	10'-0"	345
108	SPA PLUNGE	F6	W4	C1	10'-0"	308
108A	STEAM	F6	W5	C1	9'-0"	80
108B	SAUNA	F4	W8	C6	8'-0"	109
108C	MASSAGE	F4	W1	C1	10'-0"	201
109	GYM / YOGA	F7	W7	C4	11'-0"	339
110	LAUNDRY	F6	W7	C4	10'-0"	167
111	BAR & LOUNGE	F3	W4	C2	10'-0"	326
112	GUEST SUITE 3	F4	W1	C1	11'-0"	194
113	BATH	F6	W5	C1	9'-0"	132
114	GUEST SUITE 4	F4	W1	C1	11'-0"	194
115	BATH	F6	W5	C1	9'-0"	132
116	THEATER	F8	W6	C5	11'-0"	680
201	DEORHI STAIR HALL	F3	W2	C2	12'-0"	340
202	ELEV	—	—	—	—	48
203	PWDR	F1	W1	C1	10'-0"	53
204	SUITE 2	F4	W1	C1	12'-0"	238
205	BATH	F6	W5	C1	10'-0"	155
206	PRIMARY BATH	F1	W4	C3	11'-0"	286
207	RAJA MAHAL PRIMARY SUITE	F2	W1	C2	12'-0"	481
208	DRESSING	F4	W7	C1	10'-0"	255
209	MASALA KITCHEN	F6	W5	C4	10'-0"	164
210	KITCHEN	F3	W5	C1	12'-0"	738
211	FAMILY ROOM	F4	W1	C2	12'-0"	339
212	BAR	F3	W4	C2	11'-0"	167
213	SHEESH MAHAL DINING	F2	W3	C3	12'-0"	326
214	DIWAN-E-KHAS GREAT HALL	F2	W2	C3	DOME	620
215	AV	F5	W7	C4	9'-0"	64
216	MANDIR	F1	W4	C3	12'-0"	76

FINISH KEY

F1 White Makrana marble, honed
F2 White marble w/ rose-marble & pietra-dura inlay
F3 Jaisalmer gold limestone
F4 Teak plank, oiled
F5 Sealed concrete
F6 Porcelain tile, slip-resistant
F7 Rubber athletic floor
F8 Carpet on pad

W1 Araish lime plaster, polished
W2 Lime plaster with painted frescoes
W3 Thikri mirror mosaic
W4 Sandstone veneer
W5 Stone / porcelain tile full height
W6 Fabric acoustic panels
W7 Painted gypsum board
W8 Cedar T&G

C1 Painted plaster
C2 Carved teak coffers
C3 Mirror-mosaic or painted dome / vault
C4 Painted gypsum
C5 Acoustic
C6 Cedar

DOOR & OPENING SCHEDULE

NO.	FROM / TO	TYPE	WIDTH	HEIGHT
101	EXTERIOR / 101	D — carved teak pair, arched	8'-0"	10'-6"
102	EXTERIOR / 105	E — overhead, teak clad	9'-0"	8'-0"
103	EXTERIOR / 105	E — overhead, teak clad	9'-0"	8'-0"
104	105 / 102	A — single swing	3'-0"	8'-0"
105	102 / 101	A — single swing	3'-0"	8'-0"
106	103 / 101	F — elevator (by mfr.)	3'-6"	8'-0"
107	104 / GALLERY	A — single swing	2'-8"	8'-0"
108	101 / GALLERY	G — cased opening	6'-0"	9'-0"
109	116 / GALLERY	A — single swing	3'-0"	8'-0"
110	106 / GALLERY	A — single swing	3'-6"	8'-0"
111	107 / GALLERY	A — single swing	3'-0"	8'-0"
112	GALLERY / 108	A — single swing	3'-0"	8'-0"
113	108A / 108	A — single swing	2'-6"	8'-0"
114	108B / 108C	A — single swing	2'-6"	8'-0"
115	108 / 108C	A — single swing	2'-8"	8'-0"
116	GALLERY / 109	A — single swing	3'-0"	8'-0"
117	GALLERY / 110	A — single swing	3'-0"	8'-0"
118	GALLERY / 111	A — single swing	3'-0"	8'-0"
119	GALLERY / 112	A — single swing	3'-0"	8'-0"
120	GALLERY / 114	A — single swing	3'-0"	8'-0"
121	112 / 113	A — single swing	2'-8"	8'-0"
122	114 / 115	A — single swing	2'-8"	8'-0"
223	201 / GALLERY	G — cased opening	6'-0"	9'-0"
224	203 / GALLERY	A — single swing	2'-8"	8'-0"
225	202 / 201	F — elevator (by mfr.)	3'-6"	8'-0"
226	204 / GALLERY	A — single swing	3'-0"	8'-0"
227	204 / 205	A — single swing	2'-8"	8'-0"
228	207 / GALLERY	B — pair	5'-0"	8'-0"
229	206 / 207	A — single swing	3'-0"	8'-0"
230	207 / 208	A — single swing	3'-0"	8'-0"
231	209 / GALLERY	A — single swing	3'-0"	8'-0"
232	209 / 210	A — single swing	3'-0"	8'-0"
233	GALLERY / 210	A — single swing	3'-0"	8'-0"
234	210 / 211	G — cased opening	8'-0"	9'-0"
235	GALLERY / 211	G — cased opening	6'-0"	9'-0"
236	211 / 212	G — cased opening	5'-0"	9'-0"
237	212 / 213	A — single swing	3'-0"	8'-0"
238	GALLERY / 213	G — cased opening	3'-0"	9'-0"
239	214 / 213	G — cased opening	6'-0"	9'-0"
240	GALLERY / 214	H — cusped stone arch	5'-0"	10'-0"
241	GALLERY / 214	H — cusped stone arch	6'-0"	10'-0"
242	GALLERY / 214	H — cusped stone arch	5'-0"	10'-0"
243	215 / 215	A — single swing	2'-6"	8'-0"
244	214 / 216	B — pair	4'-0"	8'-0"
245	213 / EXTERIOR	C — glazed pair	6'-0"	10'-6"

WINDOW SCHEDULE

NO.	ROOM	TYPE	WIDTH	SILL
W01	109 / EXTERIOR	Fixed clerestory	8'-0"	7'-0"
W02	111 / EXTERIOR	Fixed clerestory	5'-0"	7'-0"
W03	EXTERIOR / 207	Arched casement	6'-0"	2'-6"
W04	EXTERIOR / 207	Arched casement	6'-0"	2'-6"
W05	EXTERIOR / 206	Arched casement	4'-0"	2'-6"
W06	EXTERIOR / 208	Arched casement	4'-0"	2'-6"
W07	EXTERIOR / 209	Arched casement	3'-0"	2'-6"
W08	EXTERIOR / 210	Arched casement	6'-0"	2'-6"
W09	210 / EXTERIOR	Arched casement	5'-0"	2'-6"
W10	210 / EXTERIOR	Arched casement	5'-0"	2'-6"
W11	211 / EXTERIOR	Jharokha bay — fixed + casement	8'-0"	1'-7"
W12	211 / EXTERIOR	Arched casement	4'-0"	2'-6"
W13	212 / EXTERIOR	Arched casement	4'-0"	2'-6"
W14	213 / EXTERIOR	Arched casement	5'-0"	2'-6"
W15	214 / EXTERIOR	Jharokha bay — fixed + casement	5'-0"	1'-7"
W16	214 / EXTERIOR	Jharokha bay — fixed + casement	5'-0"	1'-7"
W17	216 / EXTERIOR	Arched casement	4'-0"	2'-6"
W18	EXTERIOR / 206	Arched casement	3'-0"	2'-6"
W19	EXTERIOR / 204	Jharokha bay — fixed + casement	6'-0"	1'-7"
W20	EXTERIOR / 205	Arched casement	3'-0"	2'-6"
W21	205 / EXTERIOR	Arched casement	4'-0"	2'-6"
W22	EXTERIOR / 201	Arched casement	6'-0"	2'-6"

SCHEDULE NOTES

1. Door numbers: first digit = level (1 lower, 2 main). Openings are generated from the design model and will be renumbered in design development.
2. Exterior glazing: insulated low-E, low-reflectance (≤ 10% visible reflectance), bronze-finish thermally broken frames.
3. Hardware: hand-forged brass to the owner's selection; exterior doors keyed alike with smart-lock integration.
4. Bedroom emergency escape openings per IRC R310 — lower suites egress to the baoli court.

Landmark VENTURE GROUP

OWNER / DEVELOPER

LANDMARK VENTURE GROUP LLC

Sarvesh Joshi, Managing Partner

Paradise Valley, Arizona

sarvesh@landmarkdigi.com

ARCHITECT OF RECORD

TO BE ENGAGED — ARIZONA-REGISTERED

ARCHITECT (A.R.S. §32-101 et seq.)

NO SEAL

SCHEMATIC STUDY

NOT A REGISTRANT'S DOCUMENT

CONSULTANTS (TO BE ENGAGED)

SURVEY — ALTA / TOPOGRAPHIC
CIVIL — GRADING, DRAINAGE, ON-SITE WASTEWATER
GEOTECHNICAL
STRUCTURAL
MEP / FIRE PROTECTION
LANDSCAPE — NATIVE REVEGETATION

JOSHMAHAL

PRIVATE RESIDENCE

7080 N INVERGORDON ROAD

PARADISE VALLEY, ARIZONA 85253

APN 169-01-003D · 225,151 SF (5.17 AC)

ISSUES / REVISIONS


NO.	DATE	DESCRIPTION
0	10/18/26	SCHEMATIC DESIGN — SD-01

PHASE

SCHEMATIC DESIGN

DATE OCT 18, 2026
PROJECT JM-2610
DRAWN LVG
CHECKED —

KEY PLAN

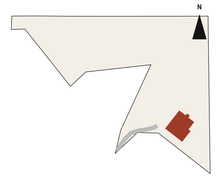

SHEET TITLE

SCHEDULES

SCALE: NTS

SHEET

A-601

12 OF 12

NOT FOR CONSTRUCTION

NOT FOR PERMIT · NOT FOR BIDDING

SCHEMATIC DESIGN — FOR OWNER REVIEW

© 2026 Landmark Venture Group LLC · JM-2610 · A-601